



RUA CARLOS DIETZSCH



1 PLANTA SUPERIOR - LAYOUT
1 : 100

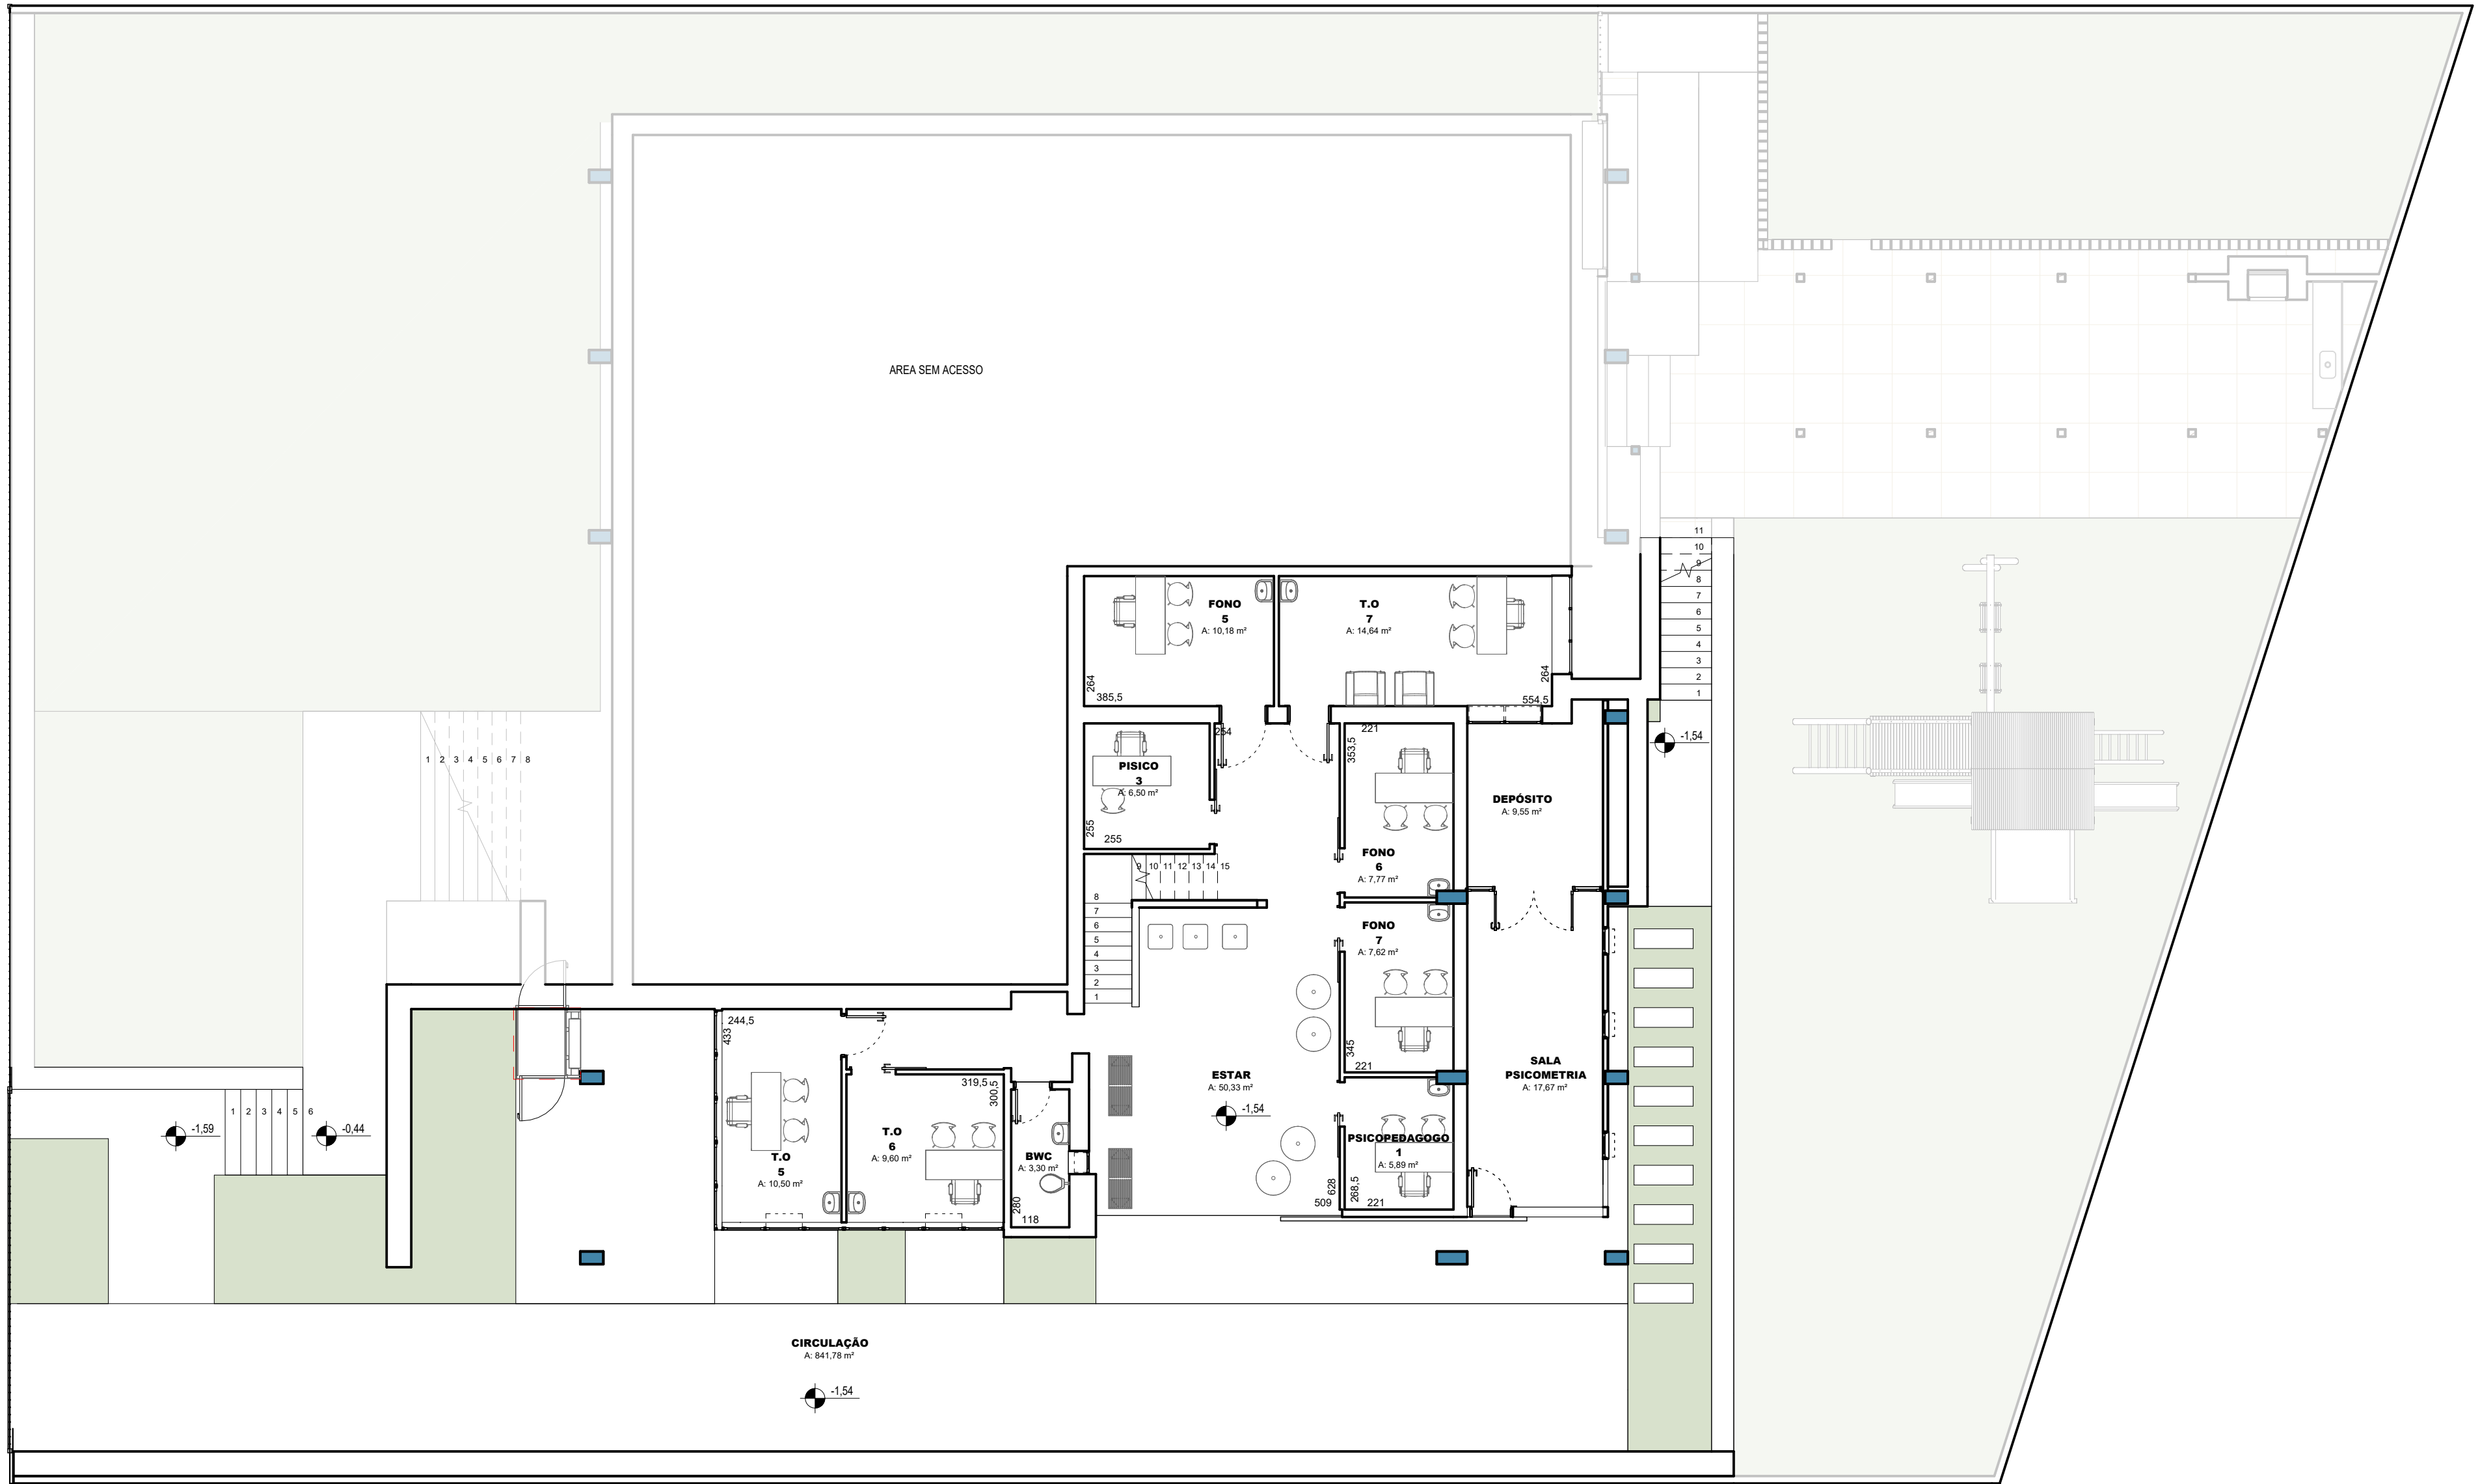

1 PLANTA INFERIOR - LAYOUT
1 : 100

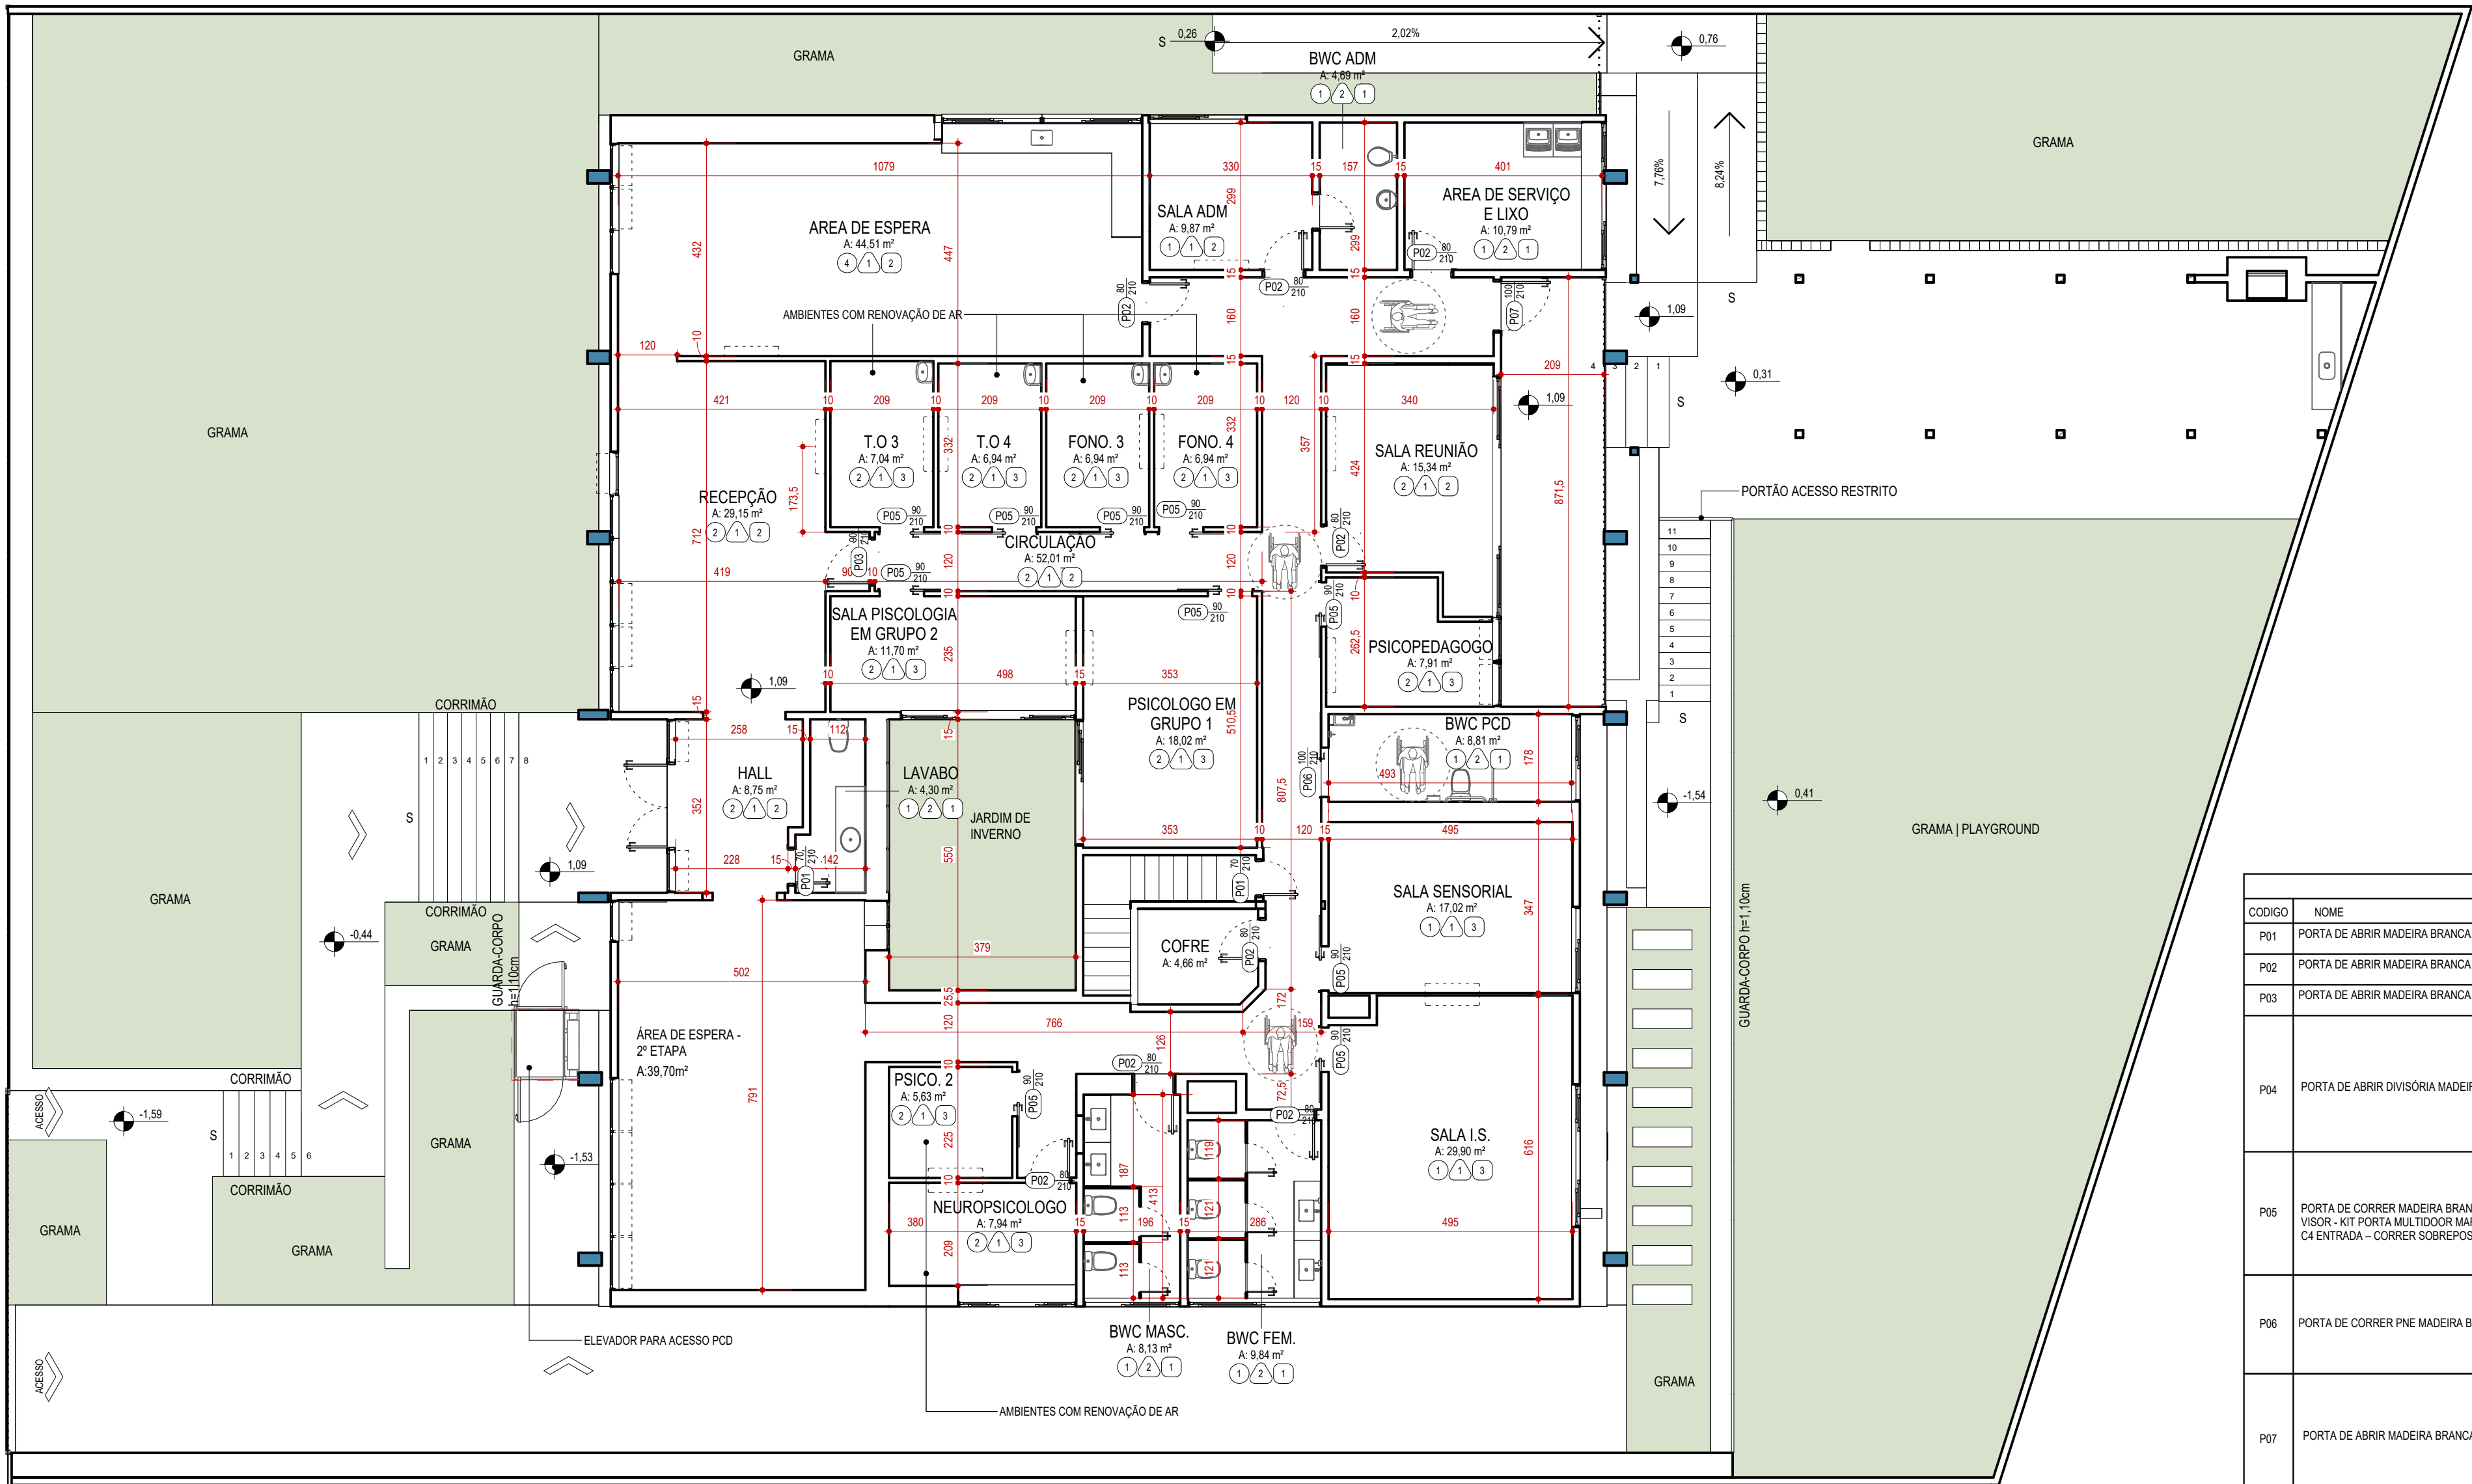

PLANTA CLINICA ARQUITETURA

ESCALA - 1 : 100


TABELA PORTAS NOVAS				
CODIGO	NOME	IMAGEM REFERENCIA	DIMENSÃO	QUANTIDADE
P01	PORTA DE ABRIR MADEIRA BRANCA		70x210	02
P02	PORTA DE ABRIR MADEIRA BRANCA		80x210	12
P03	PORTA DE ABRIR MADEIRA BRANCA		90x210	01
P04	PORTA DE ABRIR DIVISÓRIA MADEIRA BRANCA		60x180	05
P05	PORTA DE CORRER MADEIRA BRANCA COM VISOR - KIT PORTA MULTIDOOOR MARESIAS PEM- C4 ENTRADA - CORRER SOBREPOSTA		90x210	15
P06	PORTA DE CORRER PNE MADEIRA BRANCA		100x210	01
P07	PORTA DE ABRIR MADEIRA BRANCA		100x210	01

TABELA DE REVESTIMENTOS - PAREDE		
REF	DESCRIÇÃO	
1	PINTURA ACRILICA SEMI BRILHO NA COR PAPEL PICADO SUVINIL	
2	CETIM BIANCO 30x60 MATE RETIFICADO PORTOBELLO	
NA	(NÃO SE APLICA)	
TABELA DE REVESTIMENTOS - PISO		
REF	DESCRIÇÃO	
1	CETIM BIANCO 60x60 NATURAL RETIFICADO PORTOBELLO	
2	PISO LAMINADO EXISTENTE	
3	PISO LAMINADO EXISTENTE COM TATAME	
4	BLOOMY FOG 90x90 ACETINADO RETIFICADO PORTOBELL	
TABELA DE REVESTIMENTOS - TETO		
REF	DESCRIÇÃO	OBSERVAÇÕES
1	LAJE COM PINTURA LÁTEX	PÉ DIREITO:
2	FORRO DE GESSO COM PINTURA LÁTEX	PÉ DIREITO
NA	(NÃO SE APLICA)	


- 01 - Todas as medidas devem ser rigorosamente conferidas no local antes da execução do projeto, por responsabilidade do executor
- 02- Em caso de dúvidas procurar o profissional responsável pelo projeto.
- 03 - Não nos responsabilizamos por alterações na etapa de execução.

CLIENTE:	LETICIA E RICARDO VASCO	REVISÃO:	R00
TIPO DE PROJETO:	REFORMA - CLINICA ALDEIA	FASE:	EXECUTIVO
		PROJETO:	AMANDA E TATIANE

PRANCHA
028 / 07

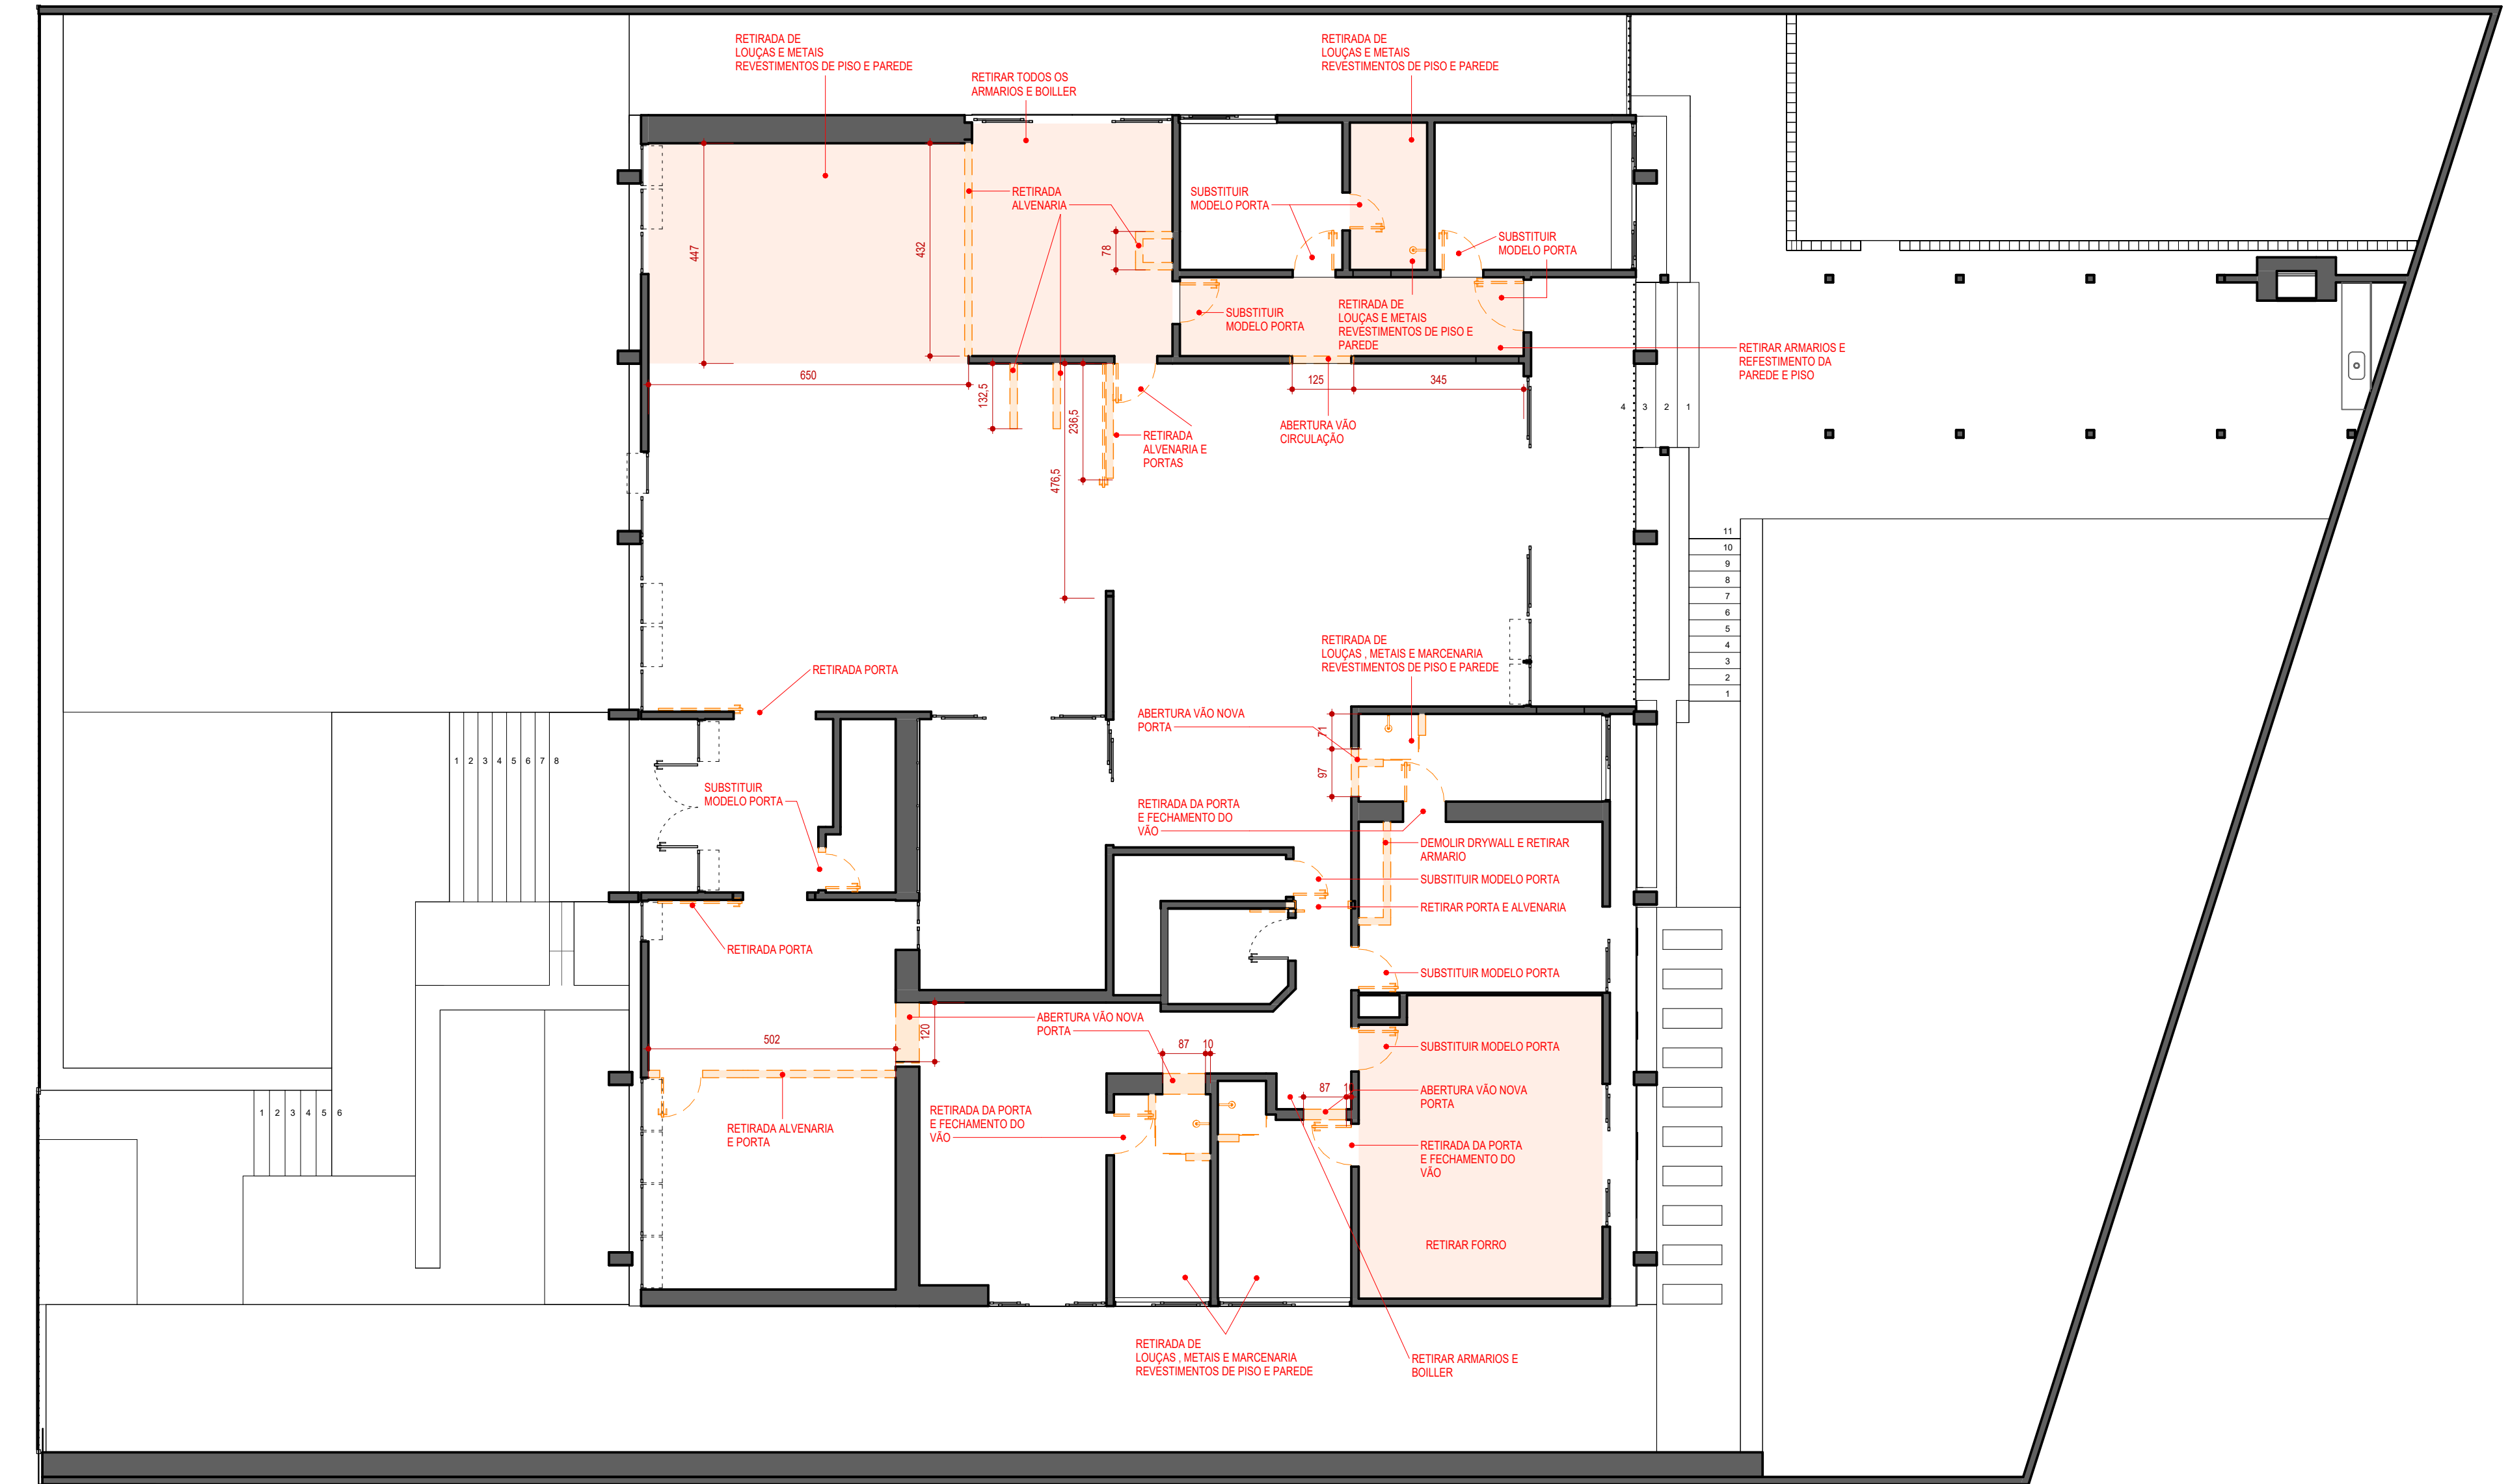


1 **PLANTA - A DEMOLIR**
1 : 100

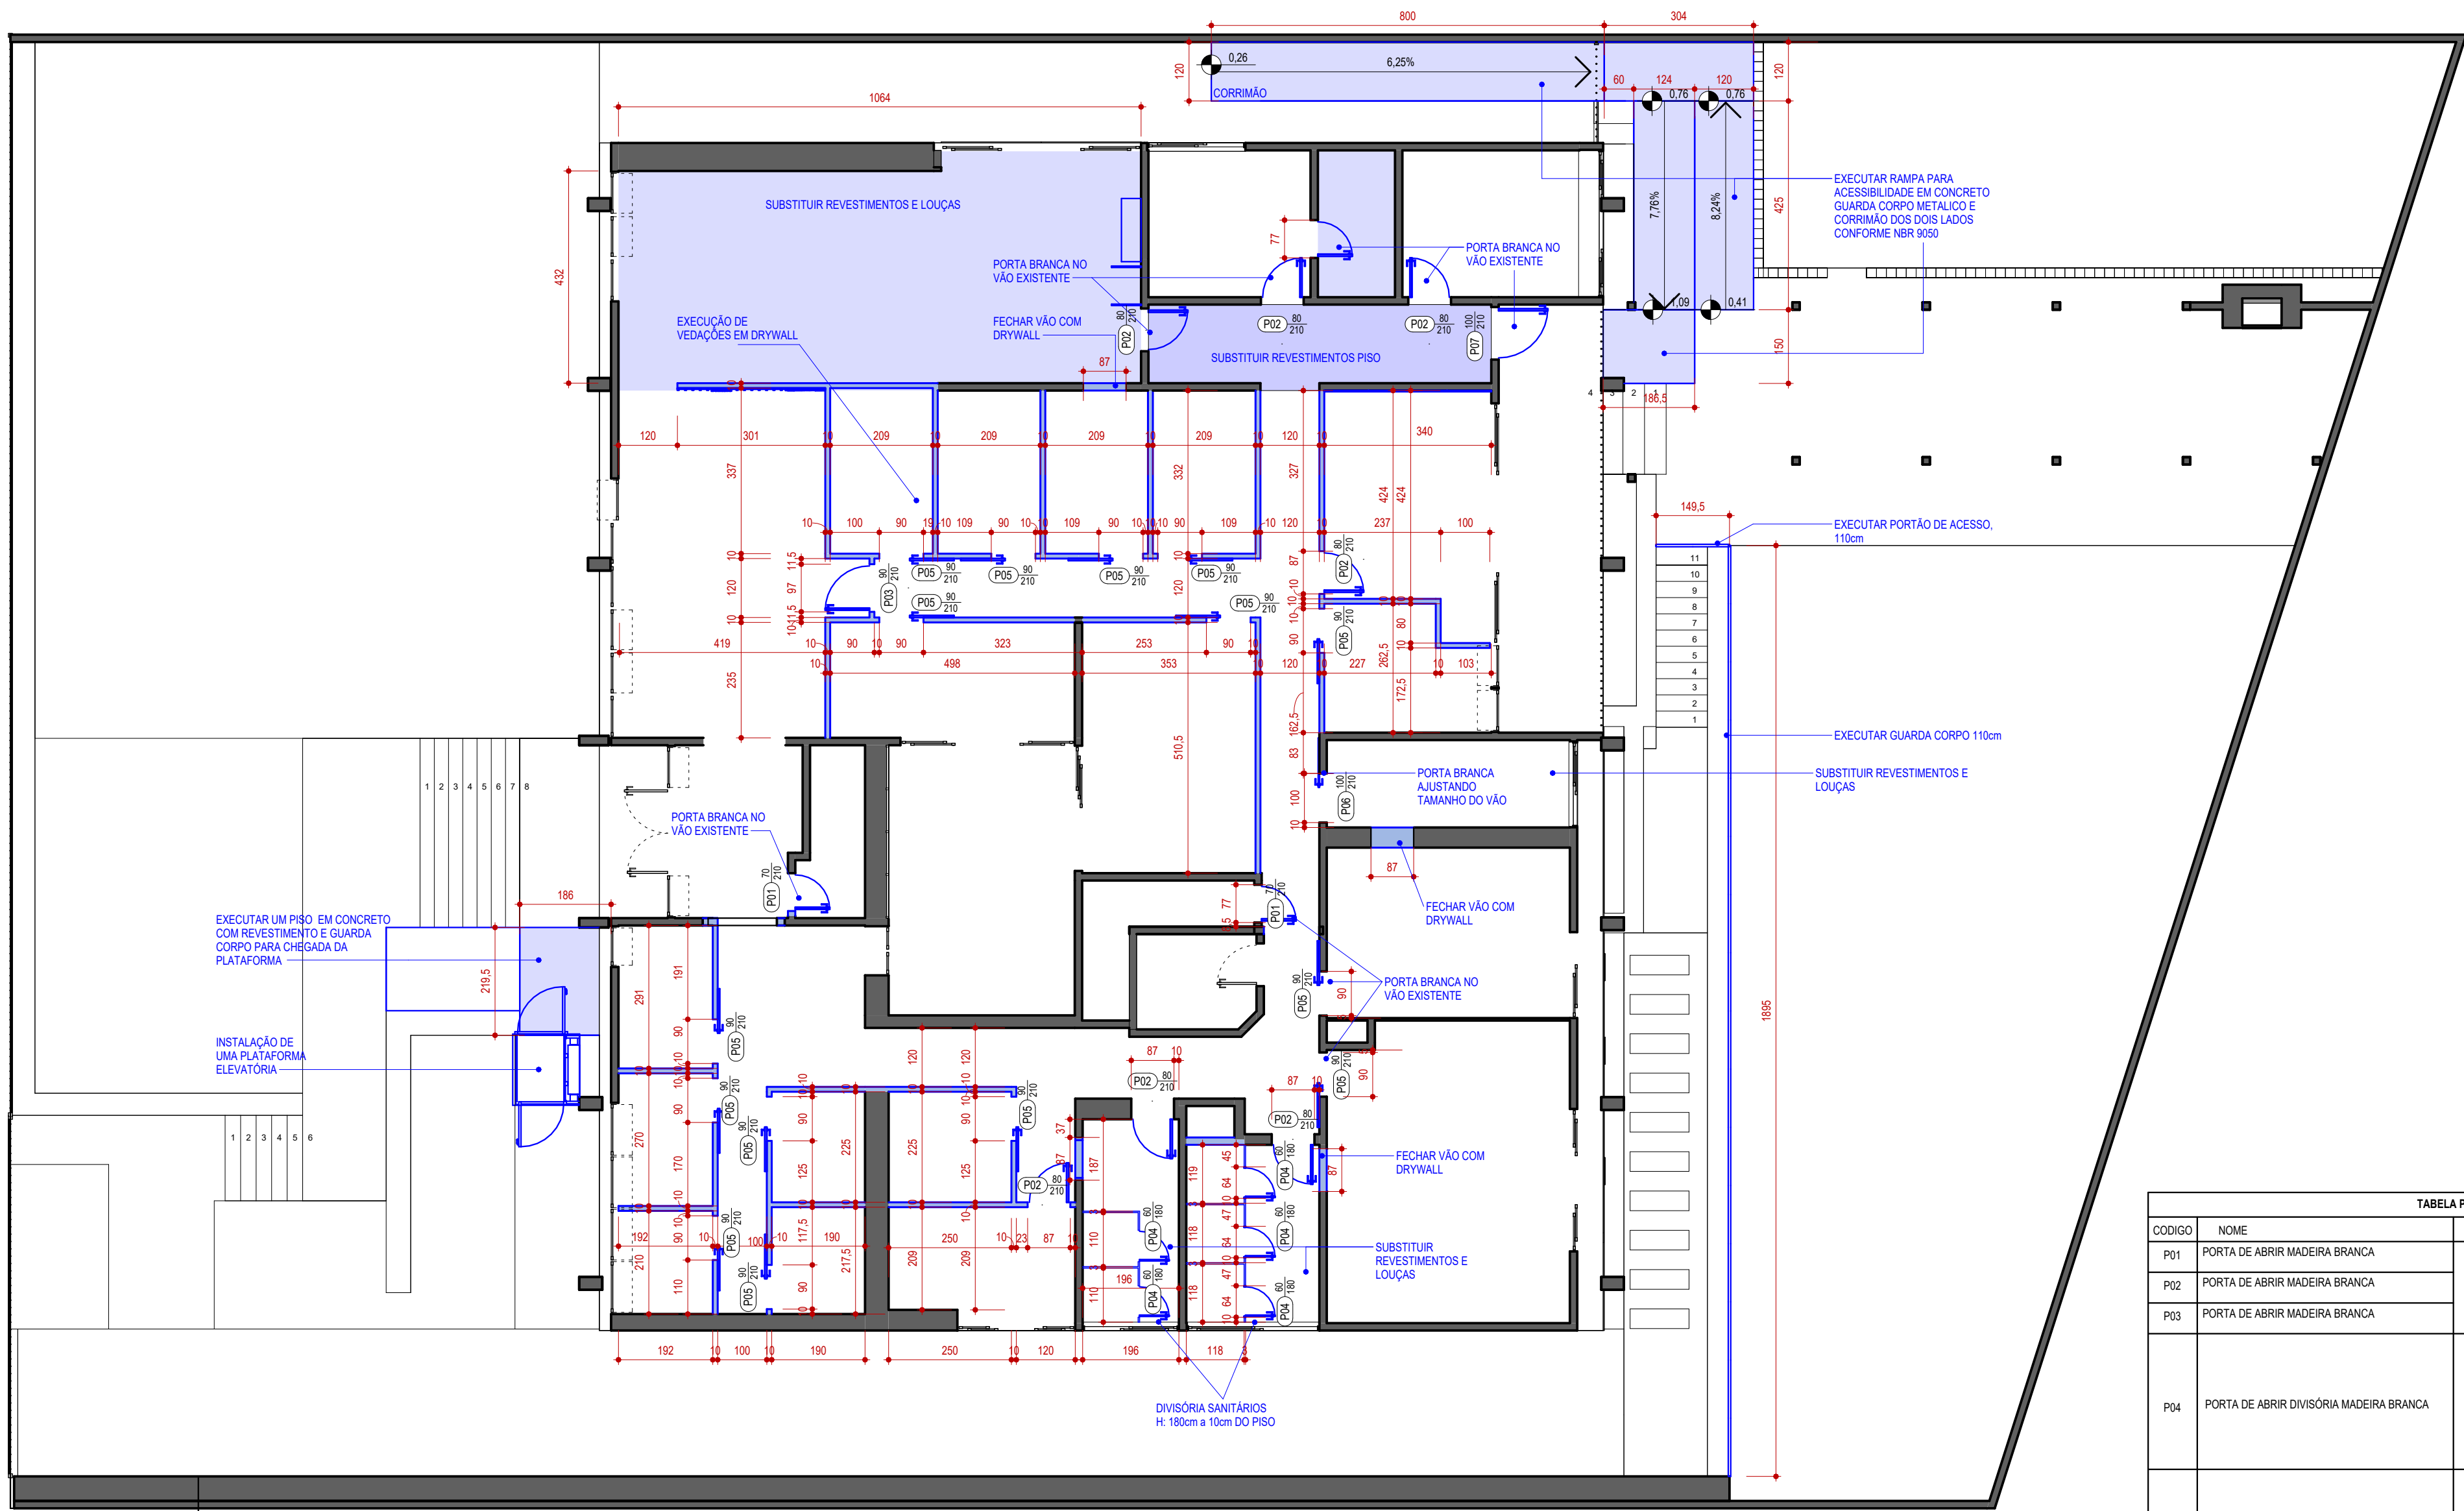

1 PLANTA A CONSTRUIR
1 : 100

TABELA PORTAS NOVAS				
CODIGO	NOME	IMAGEM REFERENCIA	DIMENSÃO	QUANTIDADE
P01	PORTA DE ABRIR MADEIRA BRANCA		70x210	02
P02	PORTA DE ABRIR MADEIRA BRANCA		80x210	12
P03	PORTA DE ABRIR MADEIRA BRANCA		90x210	01
P04	PORTA DE ABRIR DIVISÓRIA MADEIRA BRANCA		60x180	05
P05	PORTA DE CORRER MADEIRA BRANCA COM VISOR - KIT PORTA MULTIDOOR MARESIAS PEM- C4 ENTRADA - CORRER SOBREPOSTA		90x210	15
P06	PORTA DE CORRER PNE MADEIRA BRANCA		100x210	01
P07	PORTA DE ABRIR MADEIRA BRANCA		100x210	01

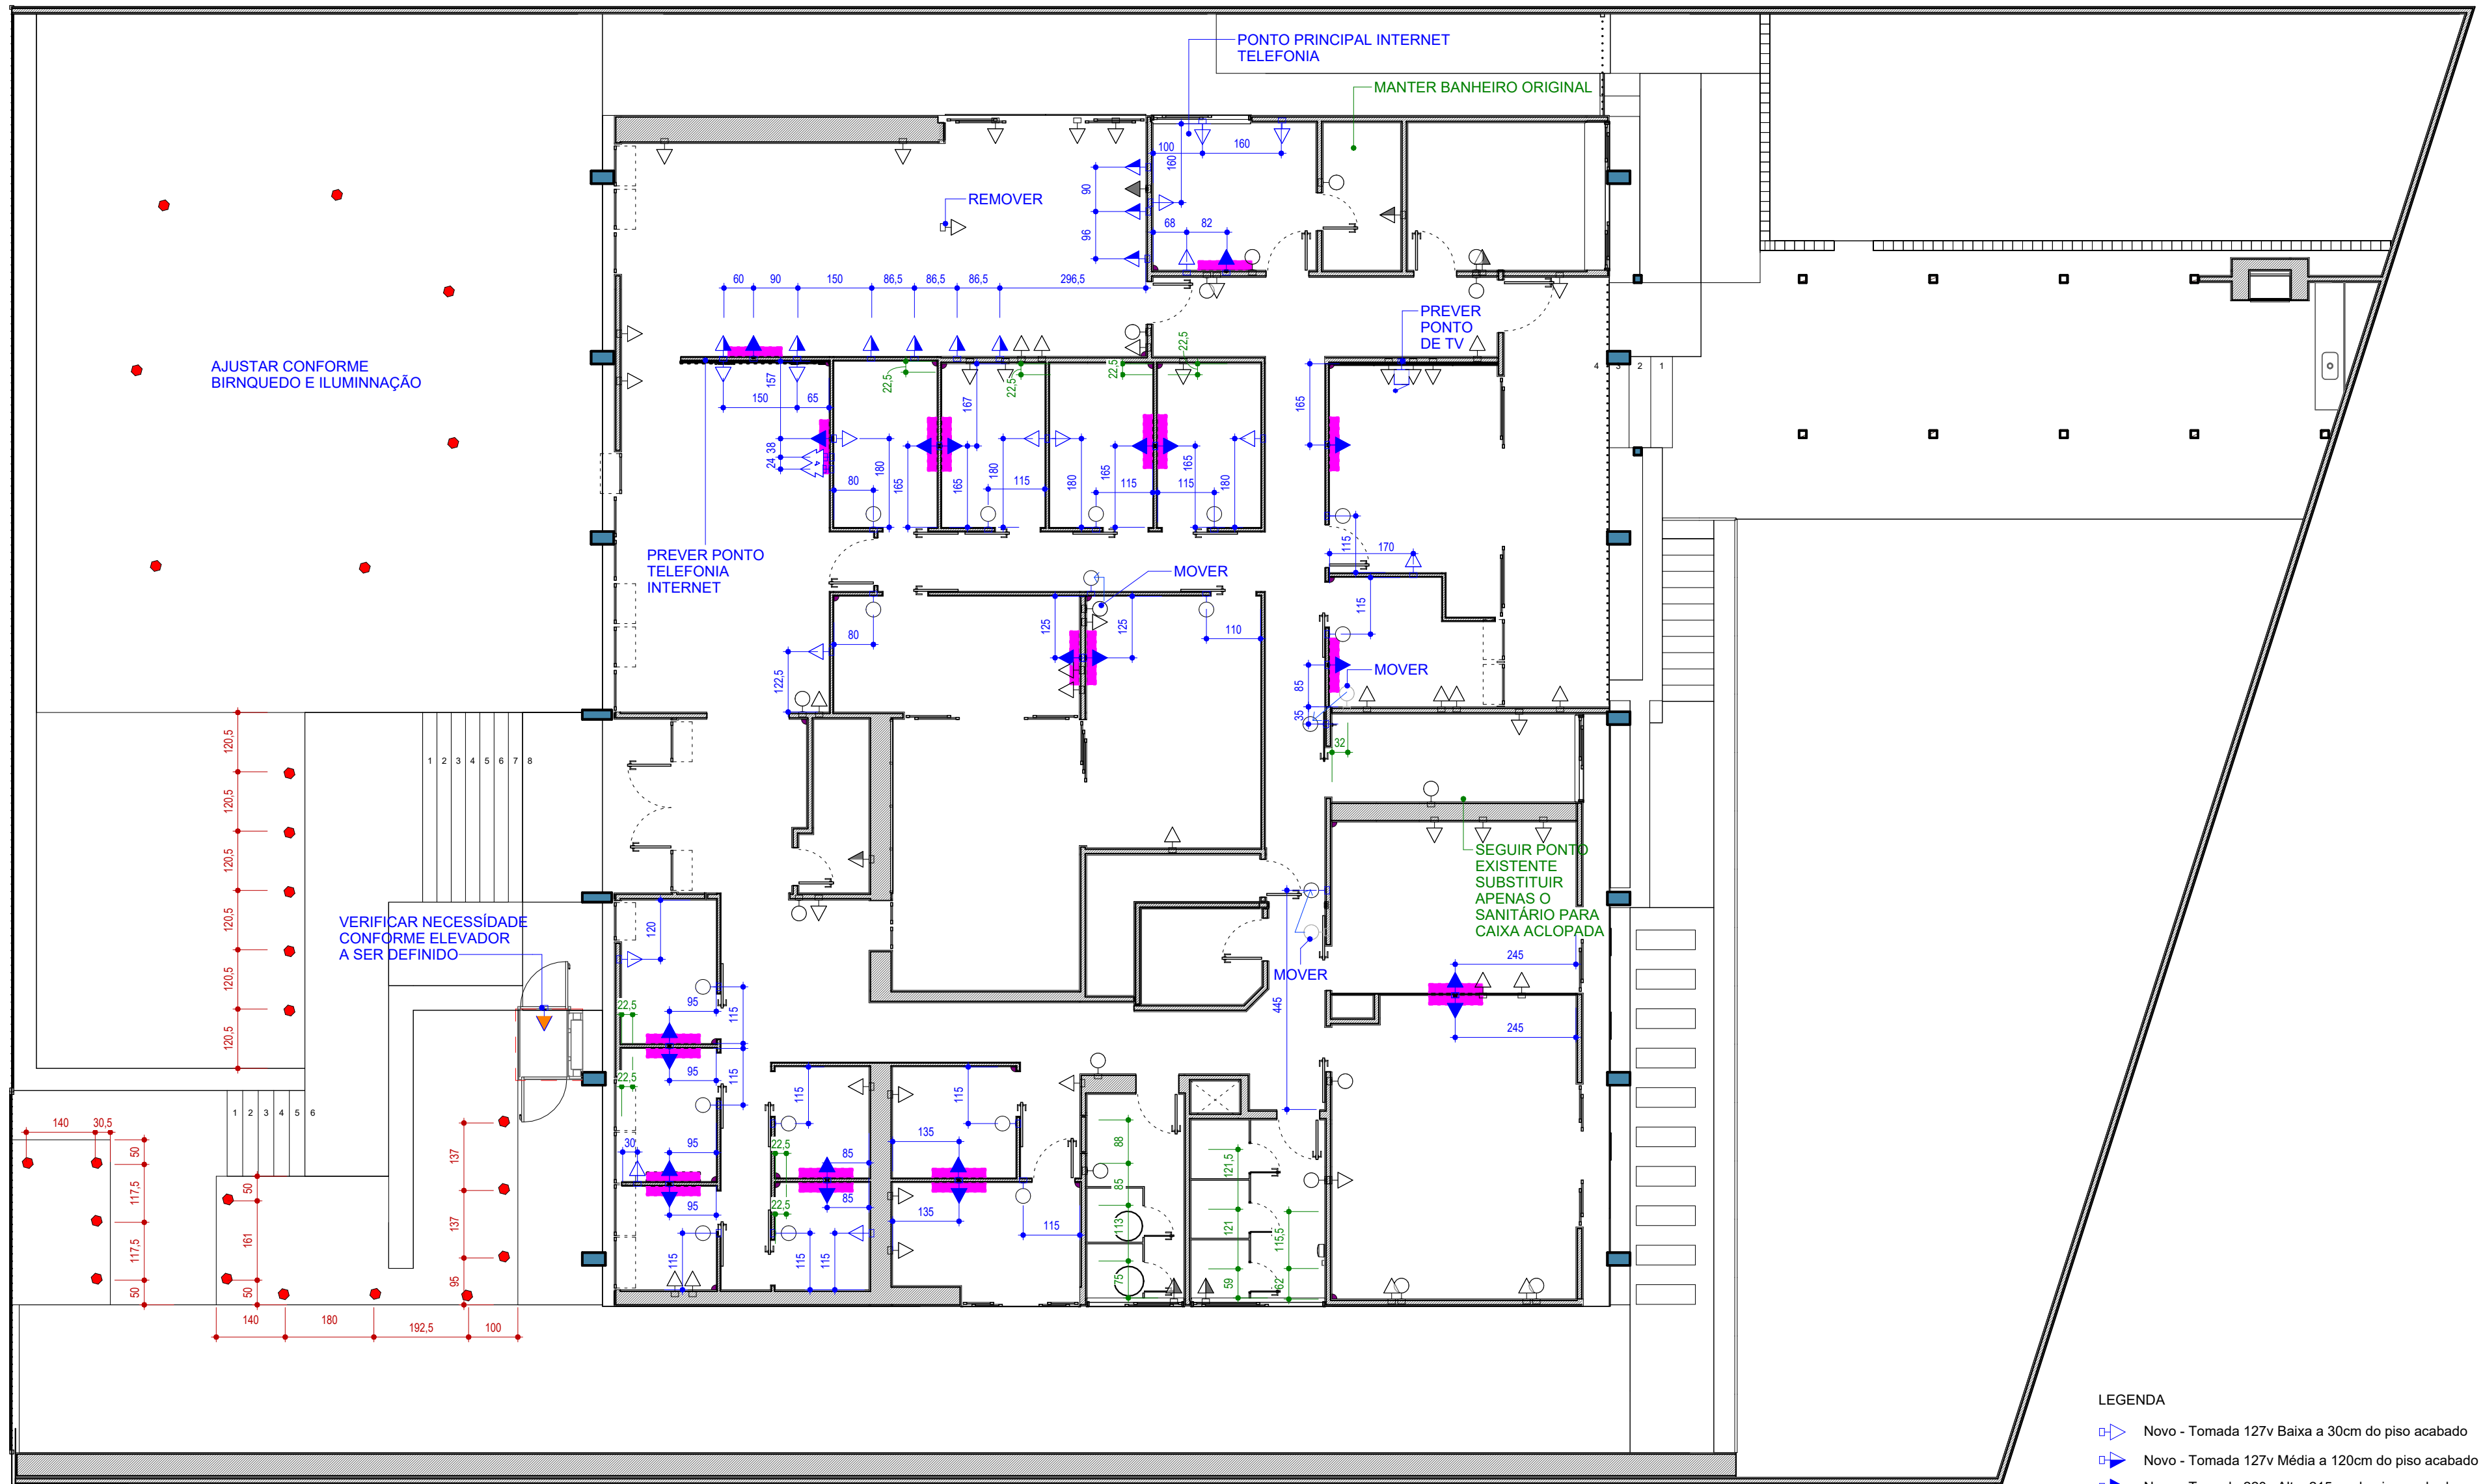


1 PLANTA - PONTOS ELÉTRICA E HIDRAULICA

ESCALA - 1 : 100

NECESSÁRIO A CONTRATAÇÃO DE PROJETO HIDRÁULICO E ELÉTICO PARA EXECUÇÃO.


LEGENDA

- Novo - Tomada 127v Baixa a 30cm do piso acabado
- Novo - Tomada 127v Média a 120cm do piso acabado
- Novo - Tomada 220v Alta 215cm do piso acabado para ar condicionado
- Novo - Tomada Elevador
- Novo - Interruptor
- Existente - Tomada Baixa a 30cm do piso acabado
- Existente - Tomada Média a 120cm do piso acabado
- Existente - Interruptor
- Novo - Split
- Novo - Hidráulica - Ponto de água fria, esgoto
- CFTV - Câmeras
- NOVO - Espeto Spot Solar 200LM Amarelo e Verde Inspire

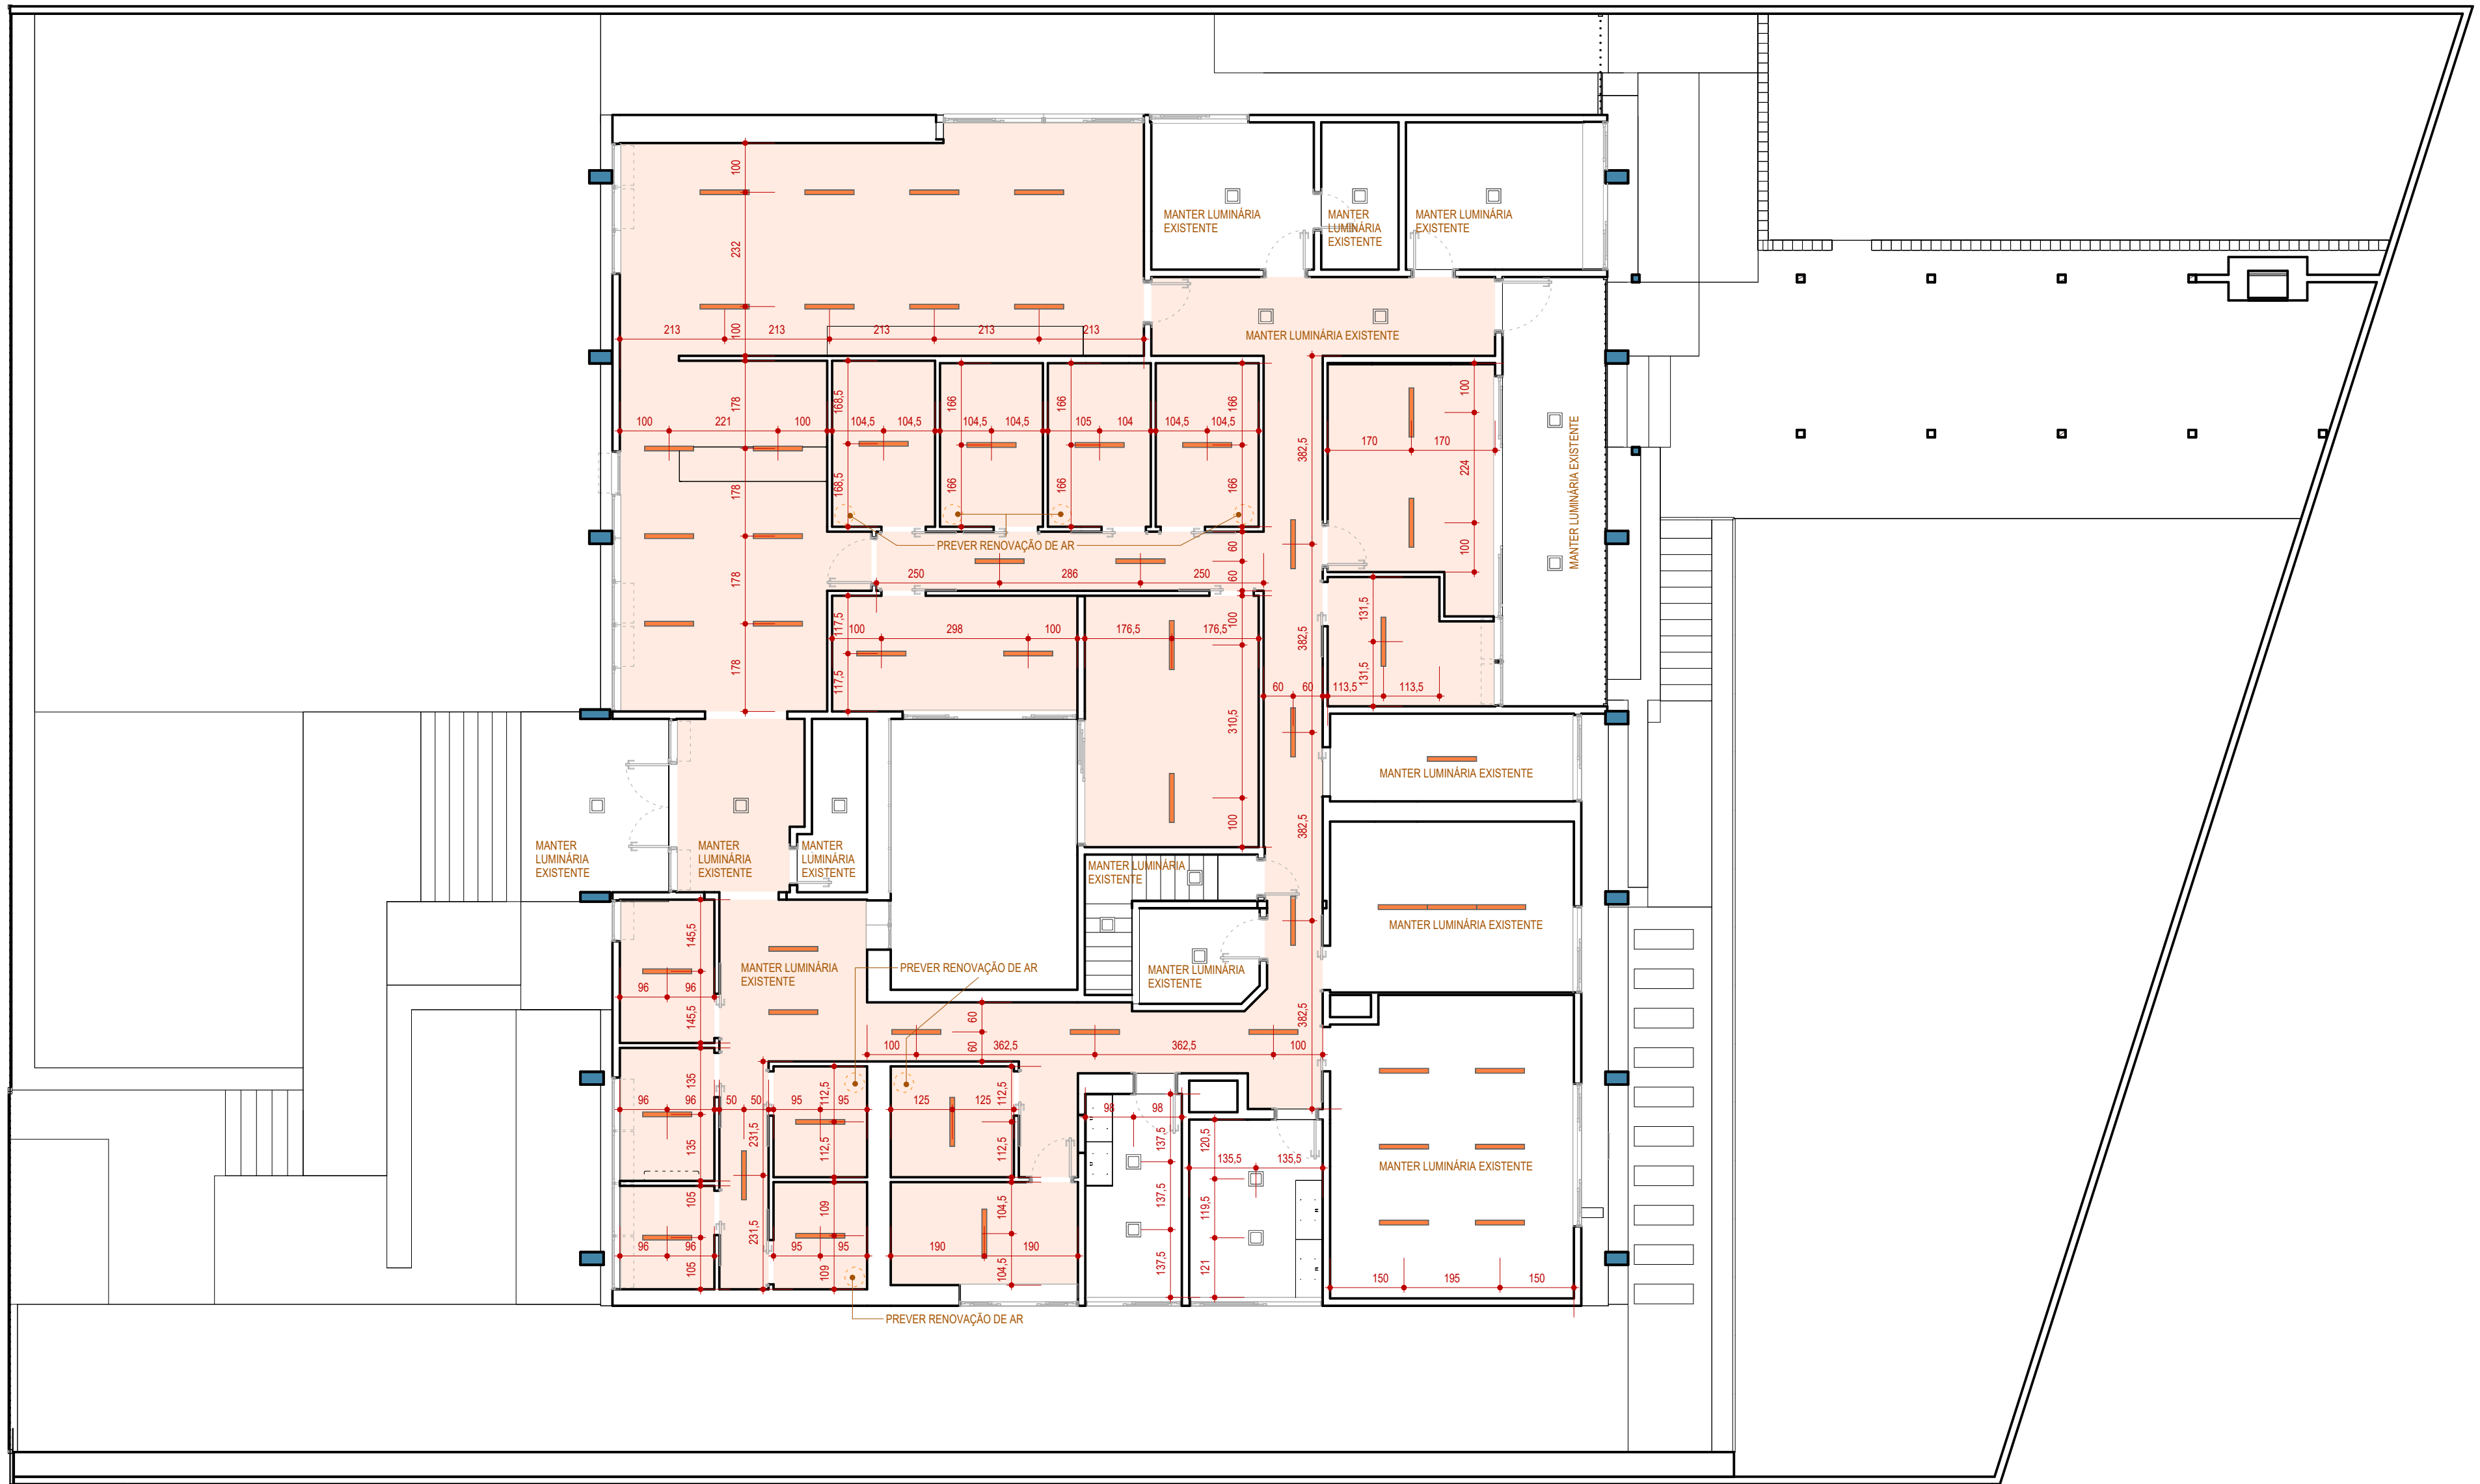


1 **PLANTA - FORRO, LUMINOTÉCNICO E RENOVACÃO DE AR**
1 : 100


- LEGENDA
- LAJE APARENTE 260cm
 - FORRO 240cm
 - LUMINÁRIA
 - LUMINÁRIA
 - RENOVACÃO DE AR

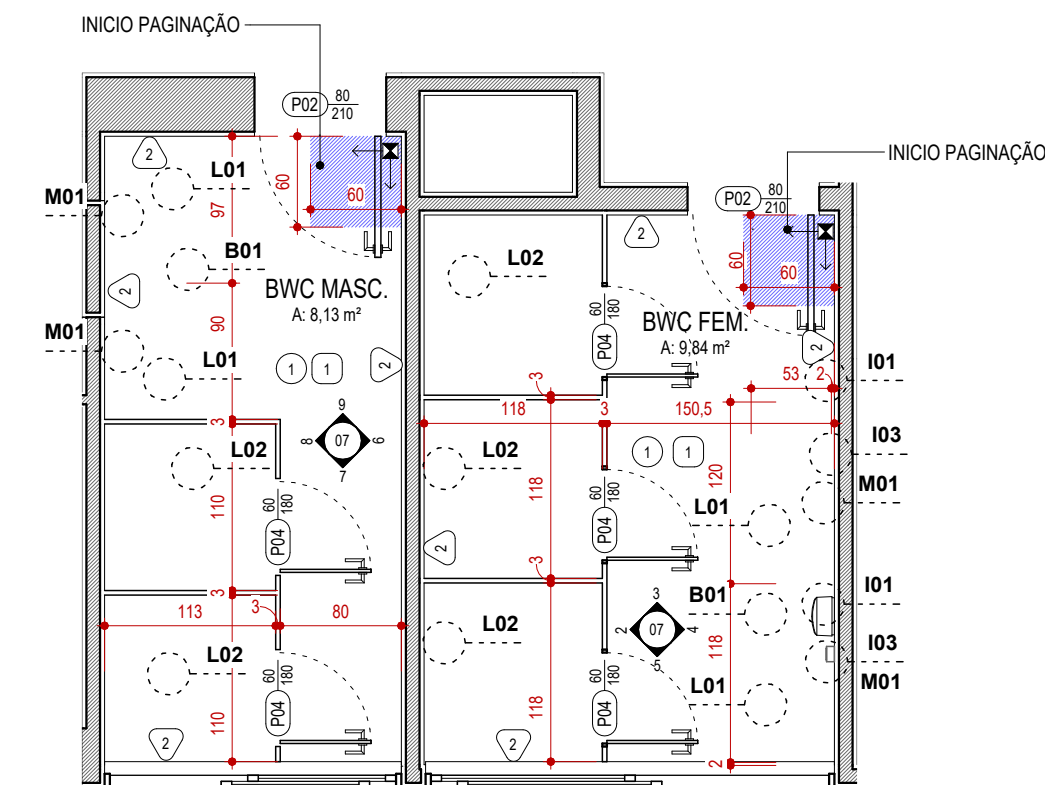


1 PLANTA BANHEIROS FEM & MAS
1 : 50

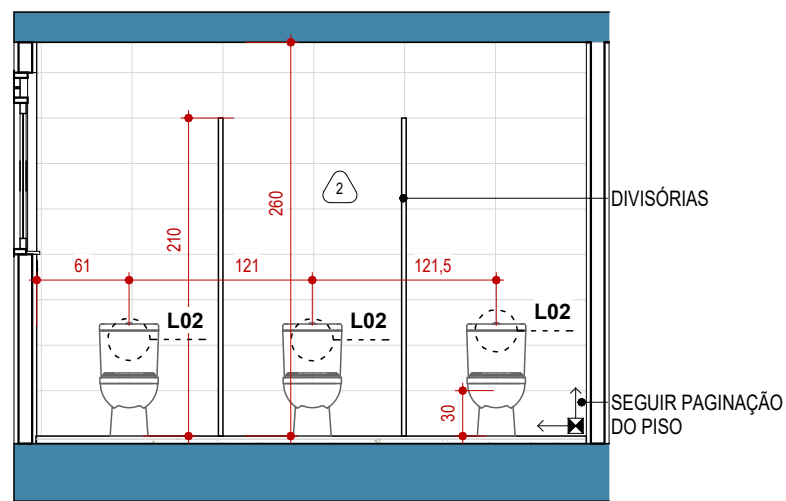


2 ELEV FEM
1 : 50

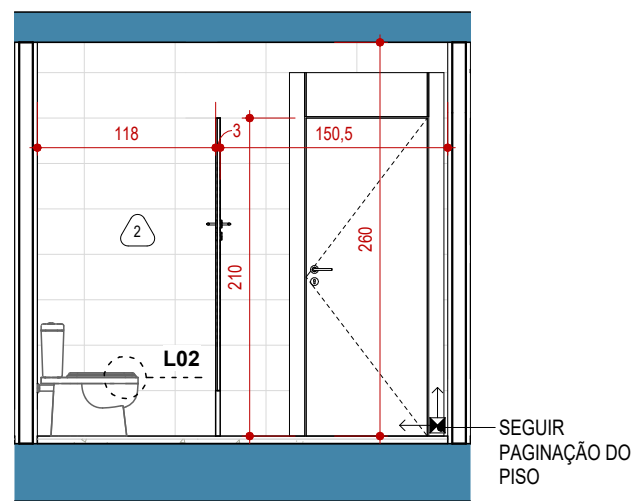


3 ELEV FEM
1 : 50

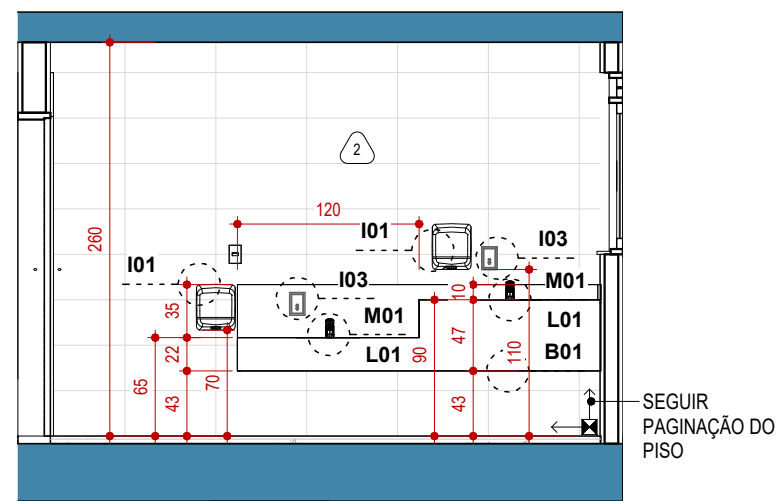


4 ELEV FEM
1 : 50

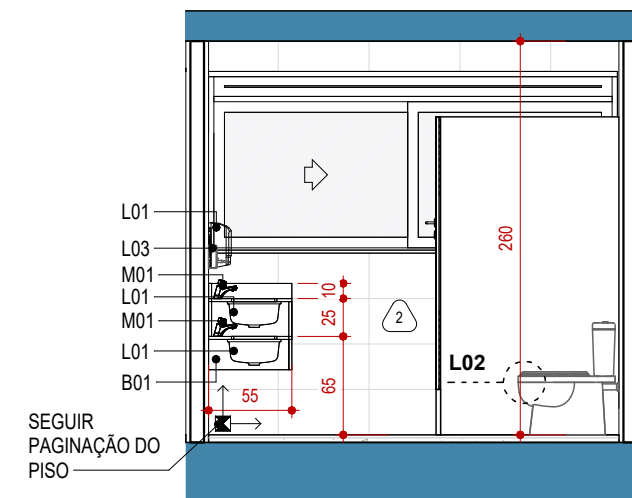


5 ELEV FEM
1 : 50

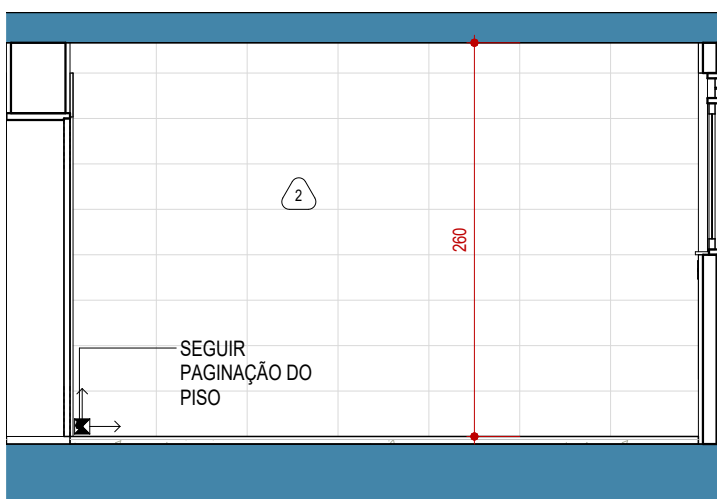


6 ELEV MASC
1 : 50

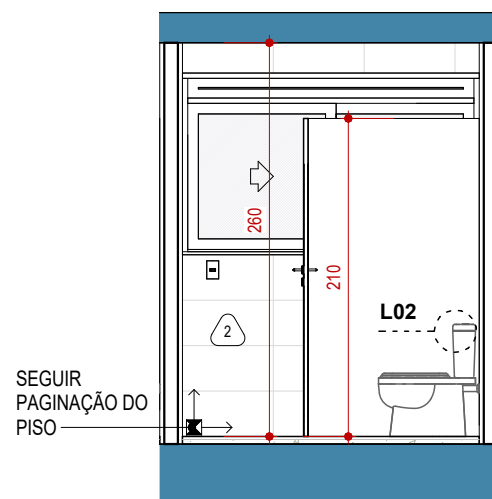


7 ELEV MASC
1 : 50

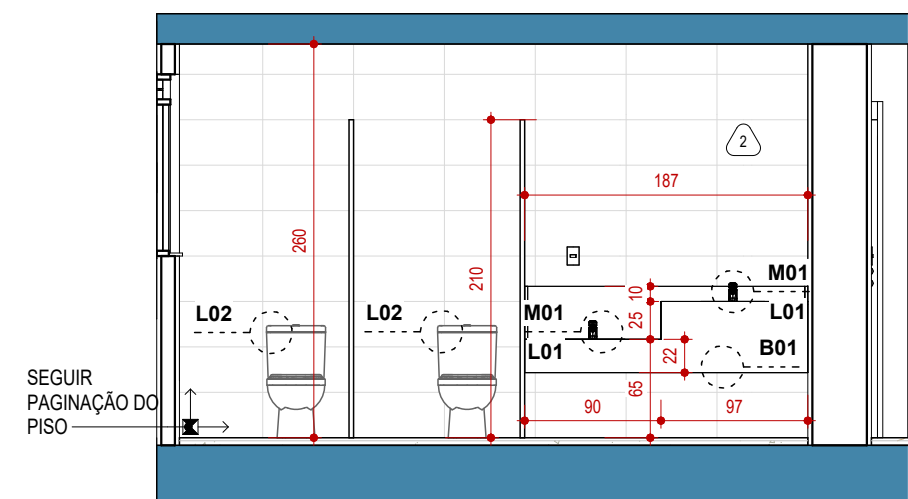


8 ELEV MASC
1 : 50

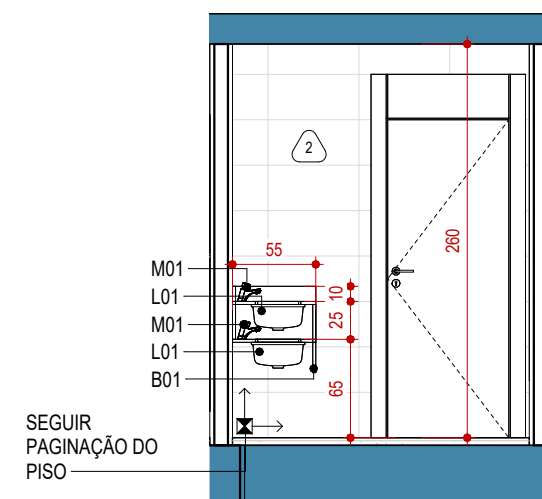


9 ELEV MASC
1 : 50

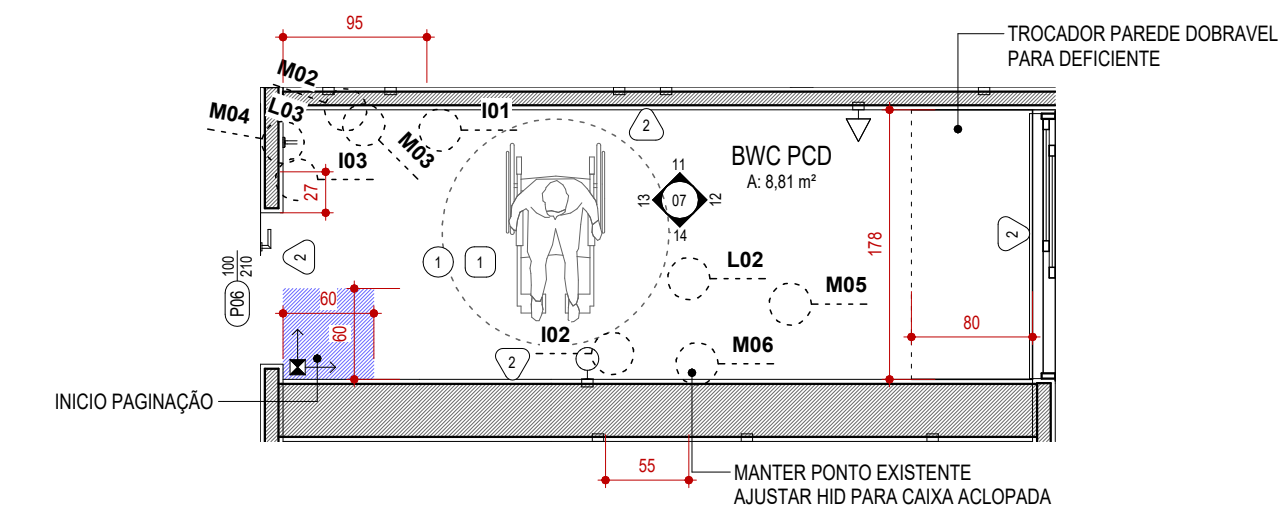


10 PLANTA BANHEIRO PCD
1 : 50

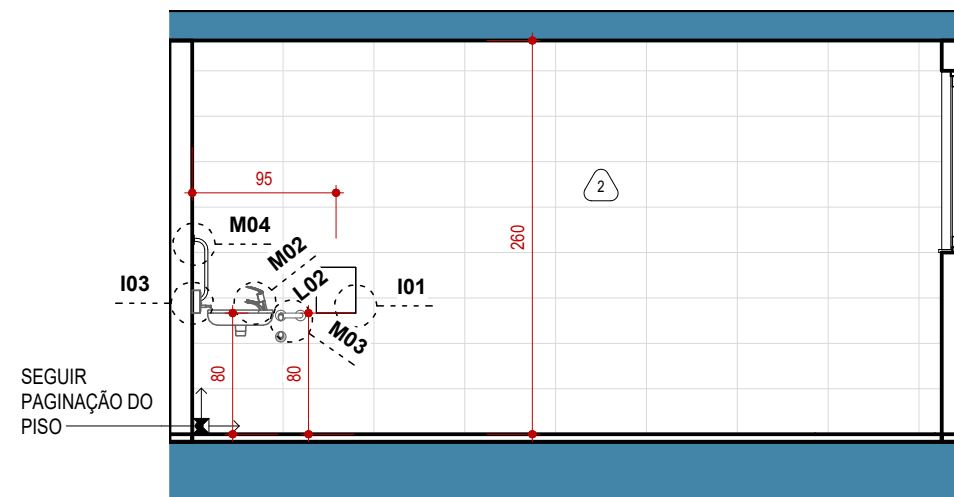


11 ELEV PCD
1 : 50

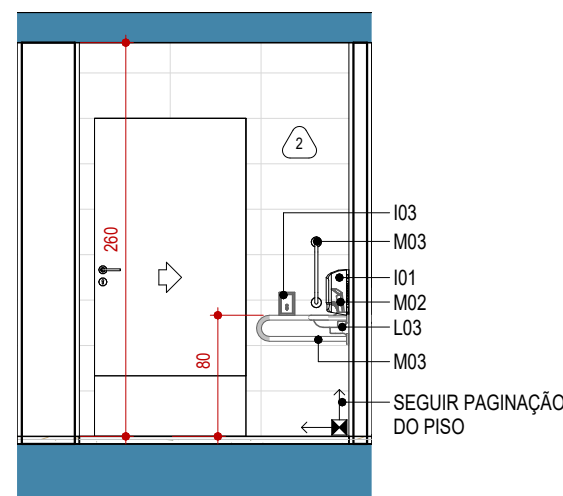

13 ELEV PCD
1 : 50

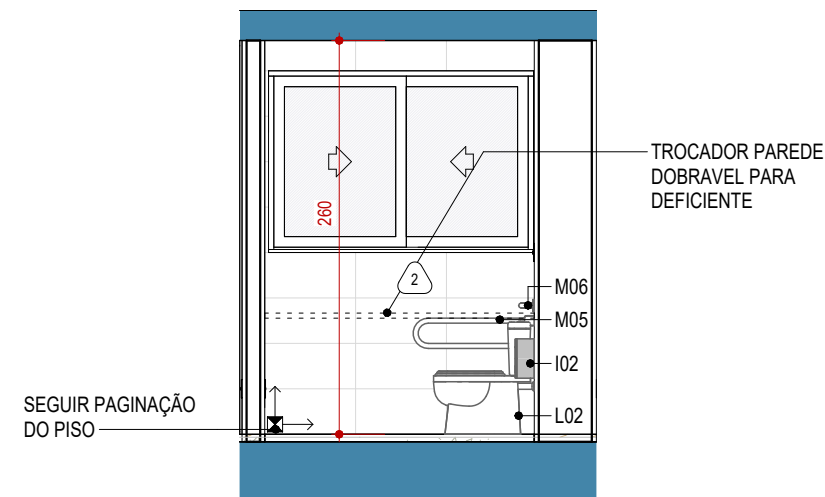

12 ELEV PCD
1 : 50

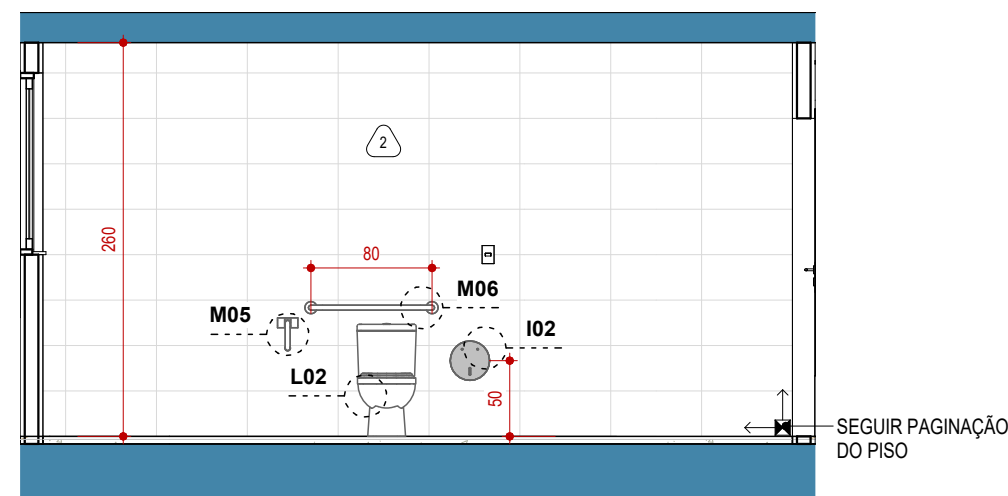

14 ELEV PCD
1 : 50

LEGENDA	
2	PARADE - CETIM BIANCO 30X60 MATE RETIFICADO PORTOBELLO
1	PISO - CETIM BIANCO 60X60 NATURAL RETIFICADO PORTOBELLO
1	TETO - LAJE COM PINTURA LATEX NA COR BANCO
B01	BANCADA EM GRANITO ITAUNAS LEVIGADO E IMPERMEABILIZADO
M01	TORNEIRA DE MESA COM FECHAMENTO AUTOMÁTICO PARA LAVATÓRIO CROMADO DECAMATIC - DECA cod:1170.C
M02	TORNEIRA DE MESA COM FECHAMENTO AUTOMÁTICO PARA LAVATÓRIO CROMADO DECAMATIC ECO - DECA cod:1173.C
M03	BARRA HORIZONTAL 30CM PARA LAVATÓRIO
M04	BARRA VERTICAL 40CM PARA LAVATÓRIO
M05	BARRA DE APOIO HORIZONTAL 80CM PARA BACIA SANITÁRIA
M06	BARRA LATERAL ARTICULADA PARA BACIA SANITÁRIA
L01	CUBA RETANGULAR DE EMBUTIR 43CM BRANCO LINHA L - DECA L.375.17 - CONSIDERAR SIFÃO FLEXIVEL
L02	BACIA PARA CAIXA ACOPLADA ASPEN BRANCO ASPEN - DECA cod: P.750.17
L03	LAVATÓRIO SUSPENSO BRANCO IZY - DECA cod: L.100.17
I01	DISPENSER PORTA PAPEL TOALHA INTERFOLHA
I02	DISPENSER PORTA PAPEL HIGIENICO ROLÃO
I03	DISPENSER PORTA SABONETE